
Schnitt A–A mit Höhenangaben

Skizze · M 1:50 (bei Druck auf A3) · Schnitt Nord–Süd durch Picknickraum, Flur mit Glasboden und Inforaum

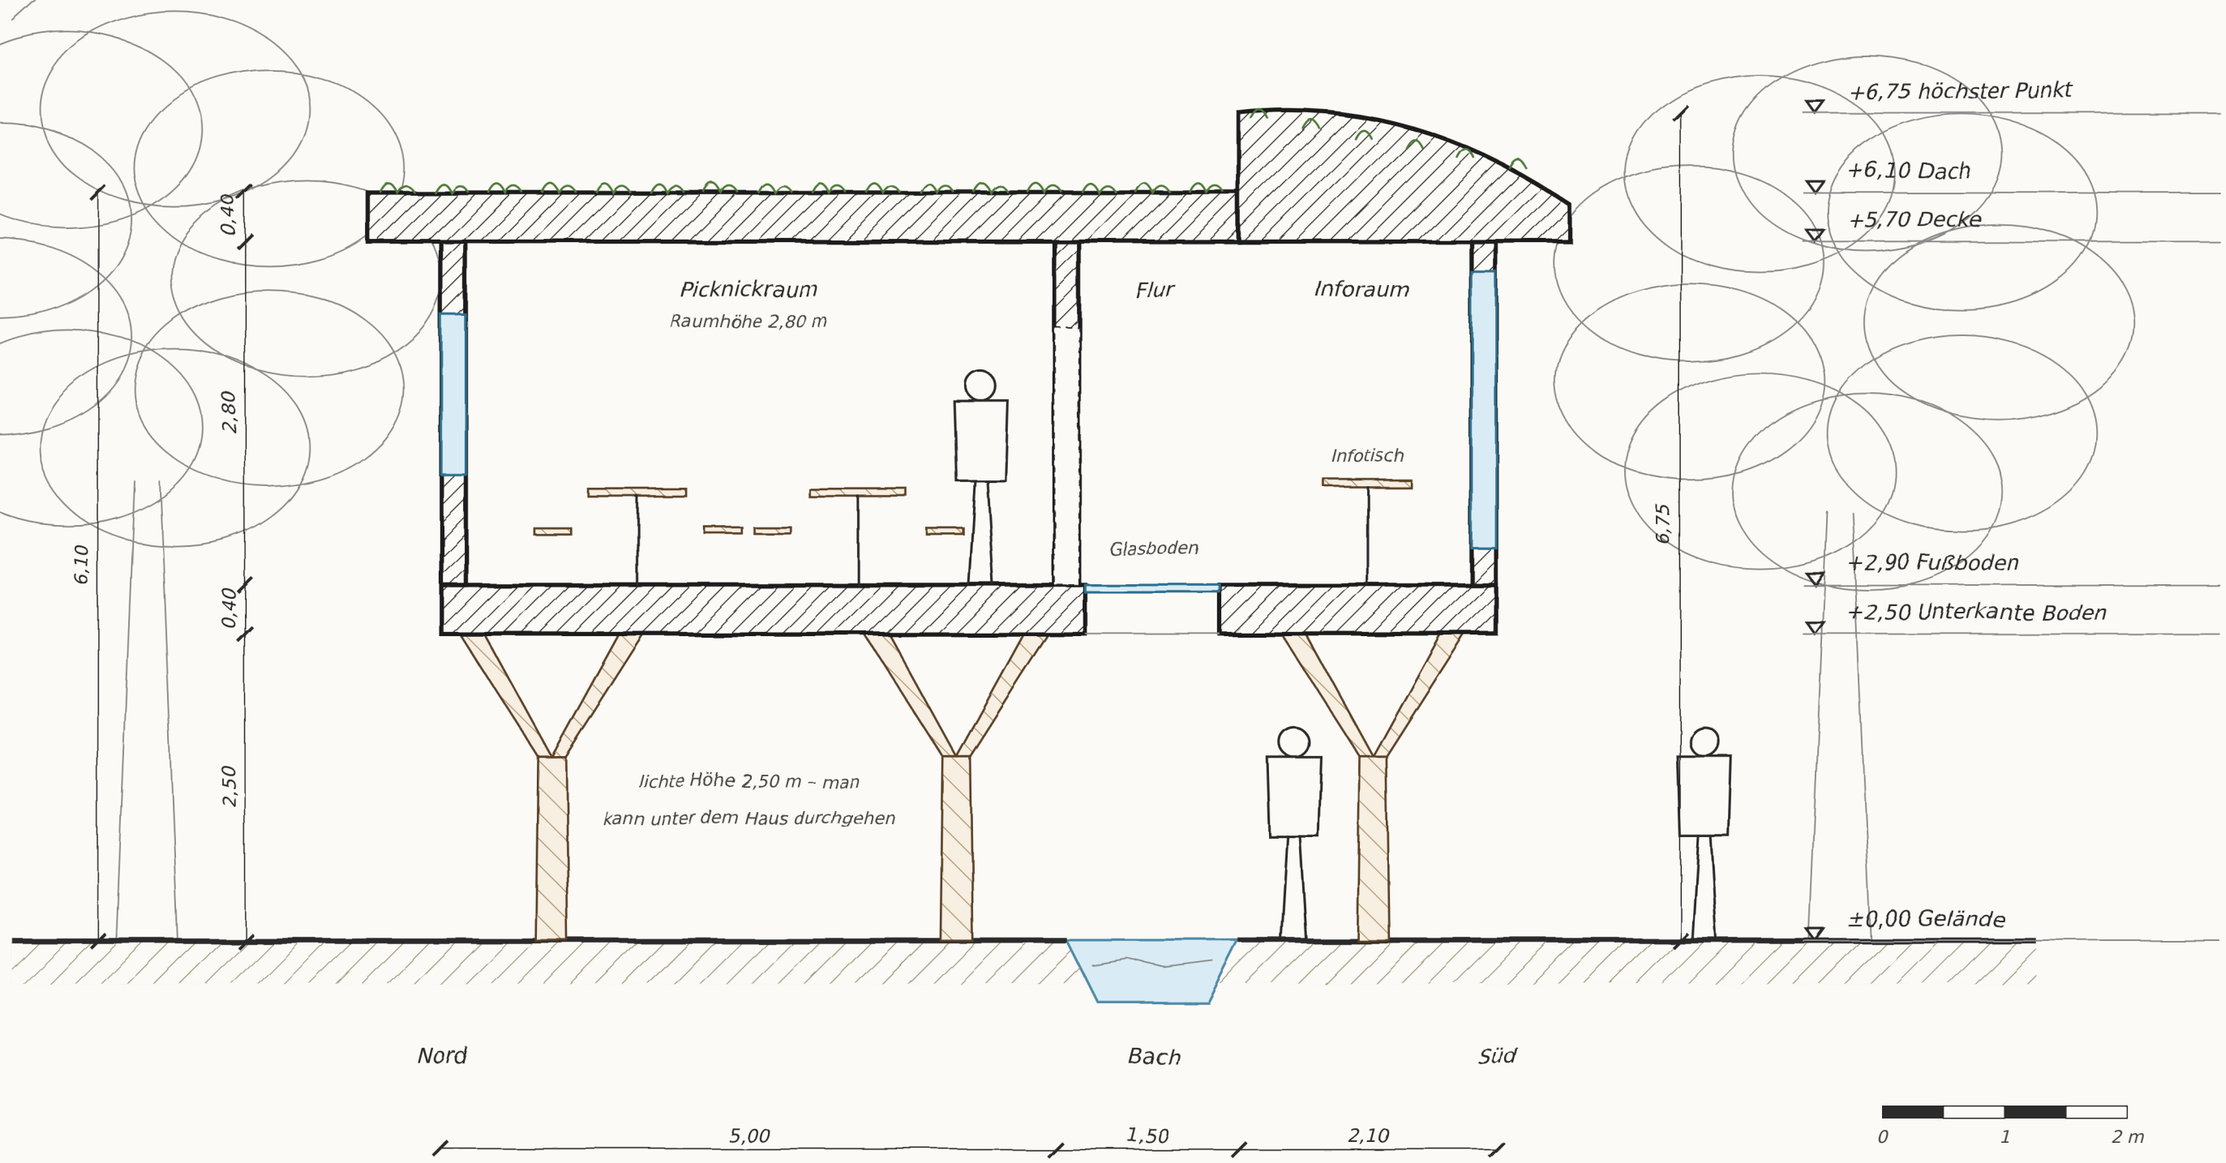

Höhen in m über Gelände (±0,00) · Holzstützen in Y-Form (Lärche) · Boden 40 cm · Raumhöhe 2,80 m · Gründach 40 cm
Bogentreppe: 17 Stufen × 17 cm = 2,89 m ≈ +2,90 · Gesamthöhe 6,10 m, höchster Punkt (Inforaum) 6,75 m